




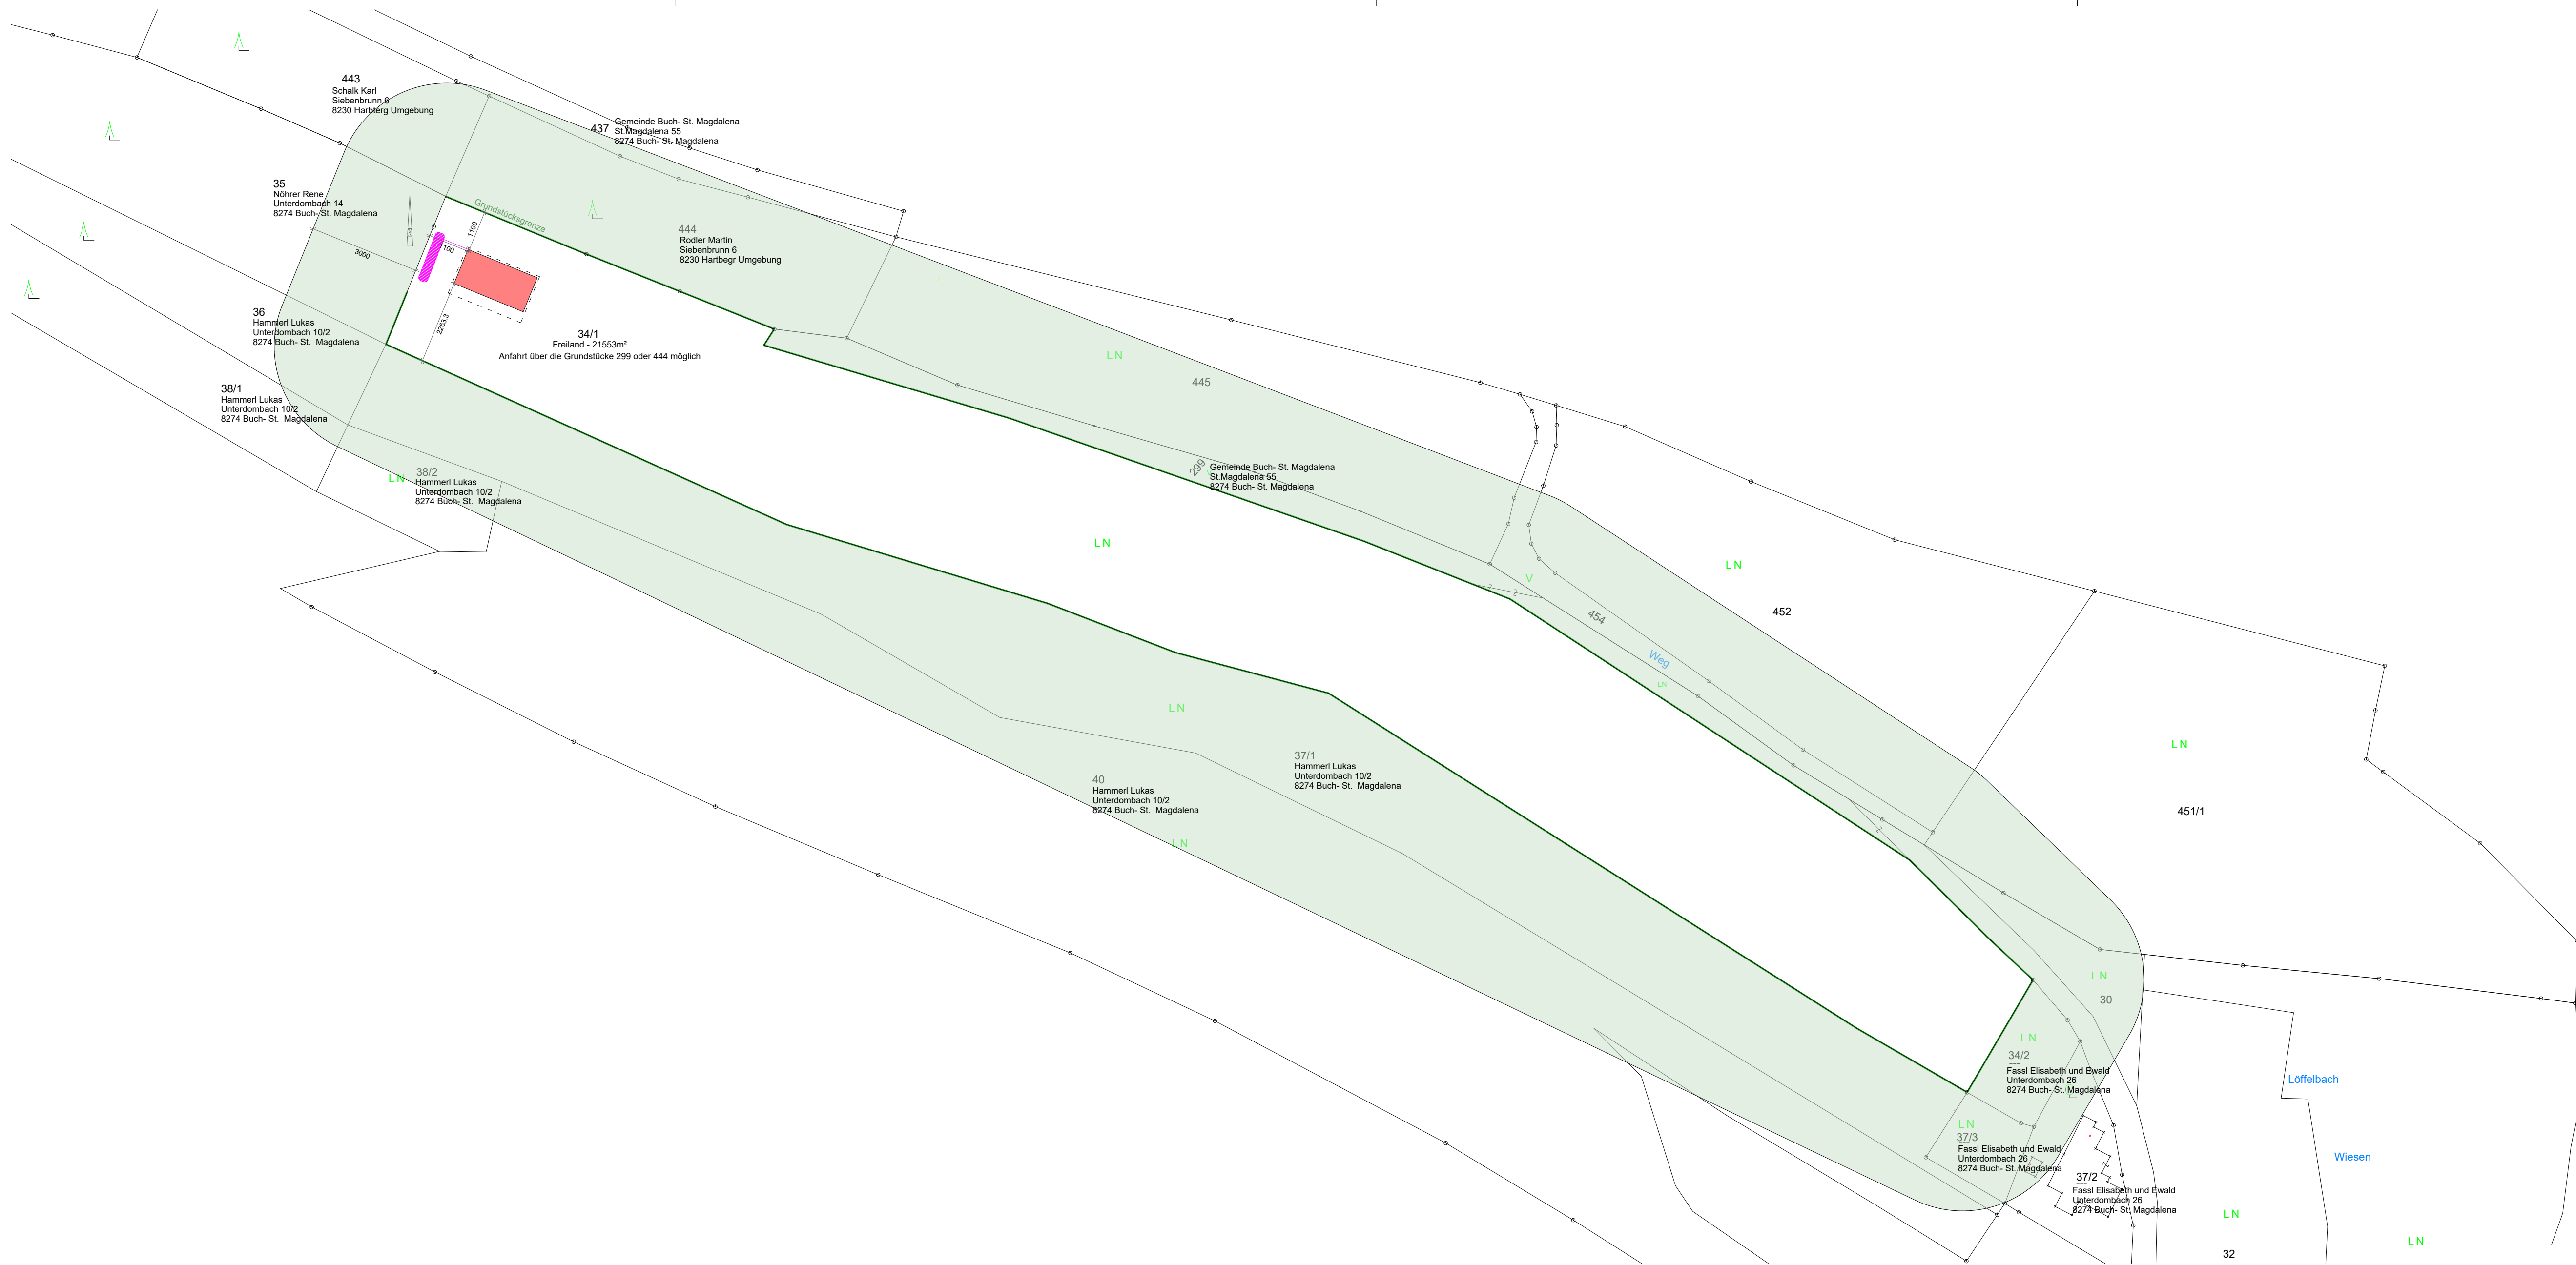


BRUTTOGESCHOSSFLÄCHE

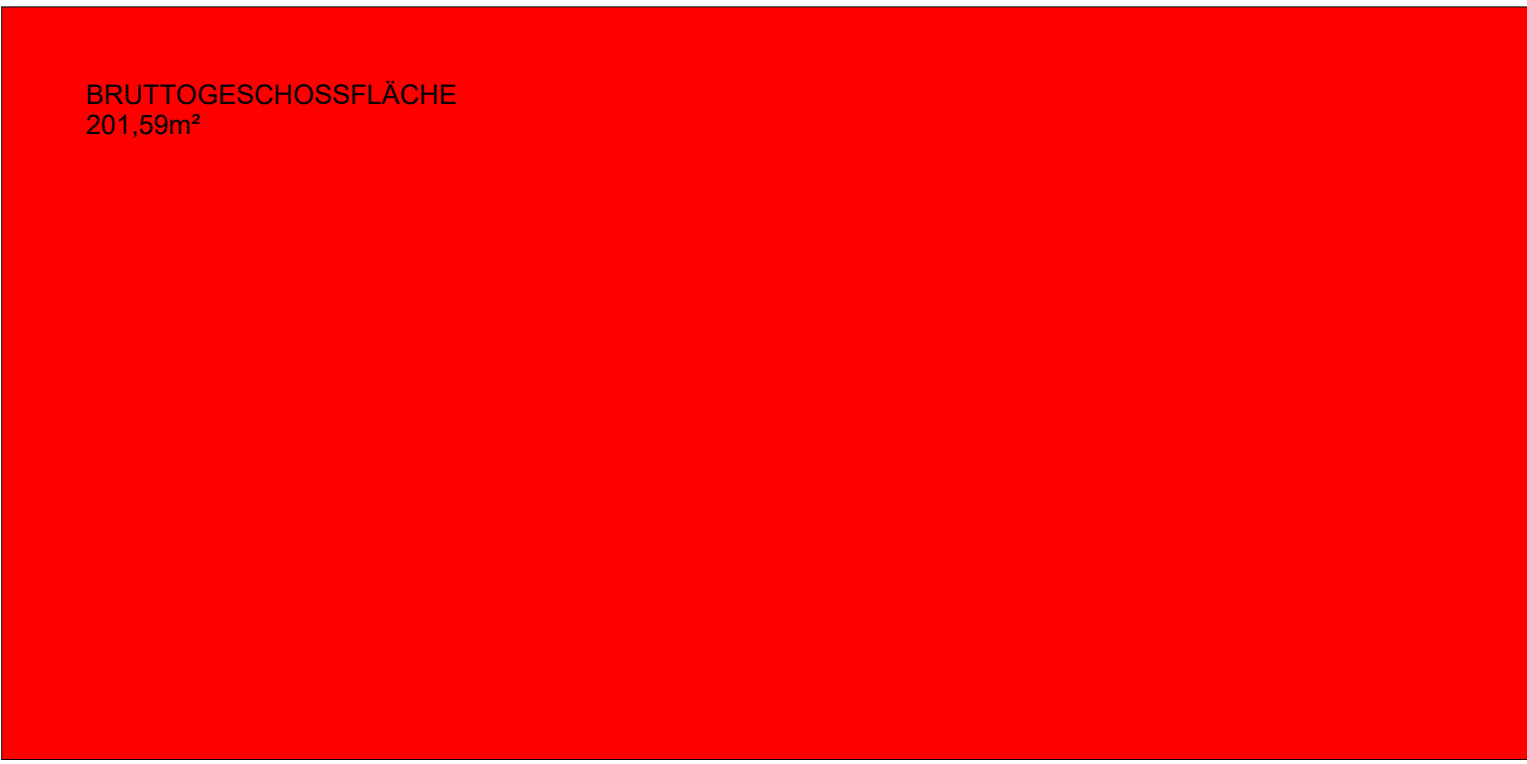


ANSICHT NORD-WEST

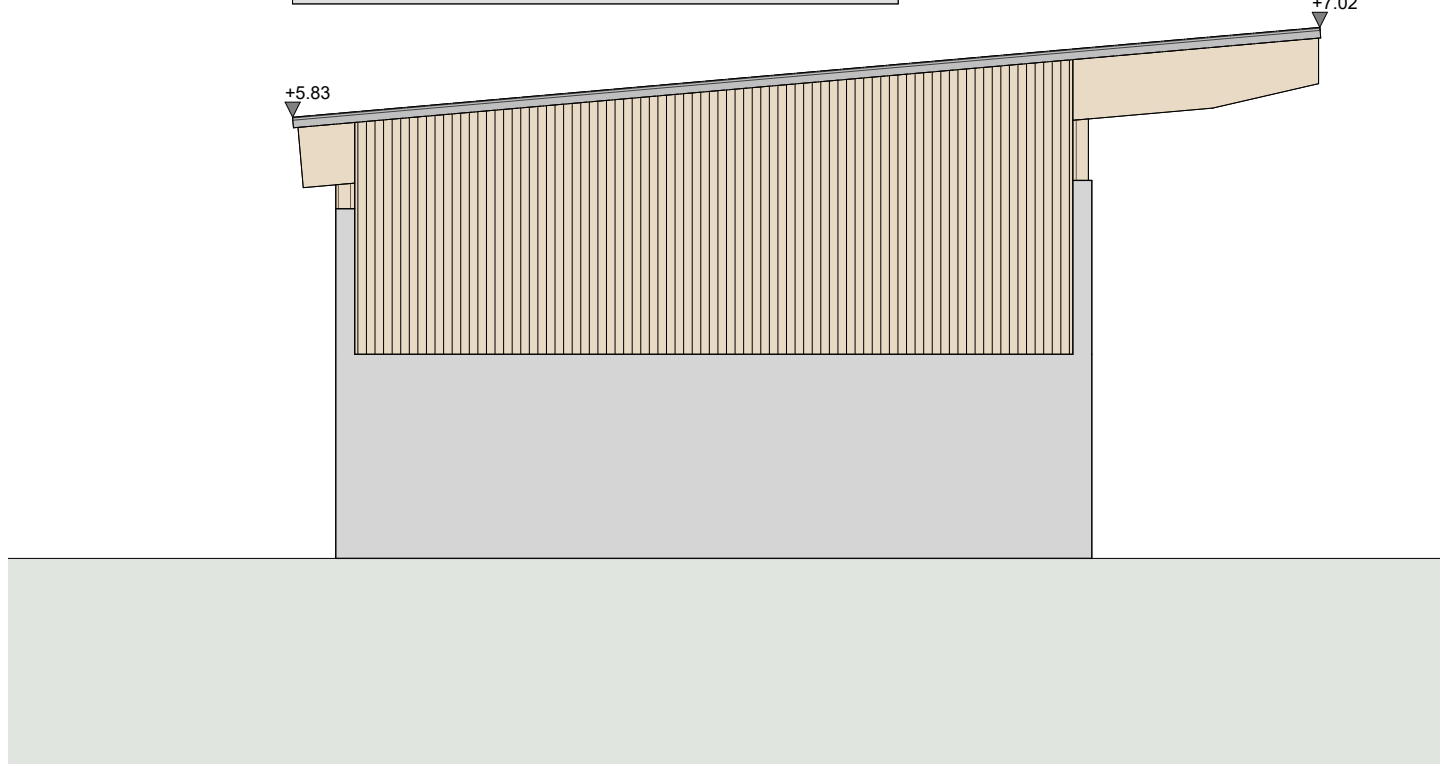


ANSICHT SÜD-WEST

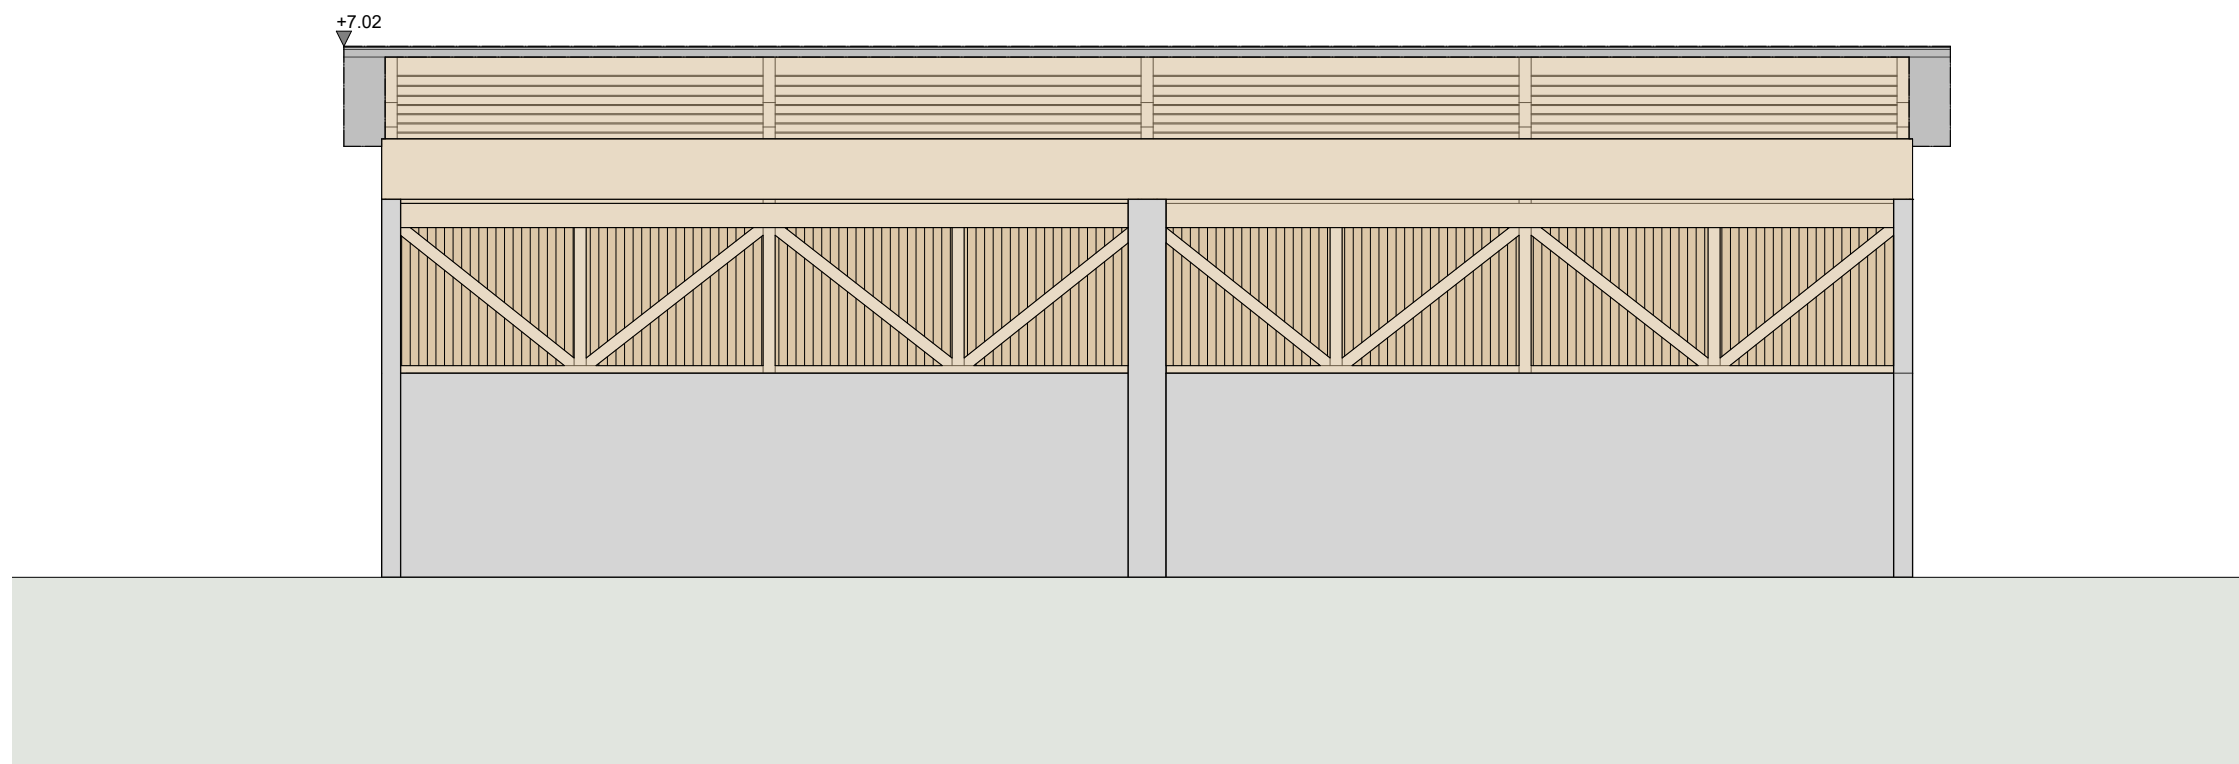



ANSICHT NORD-OSTEN

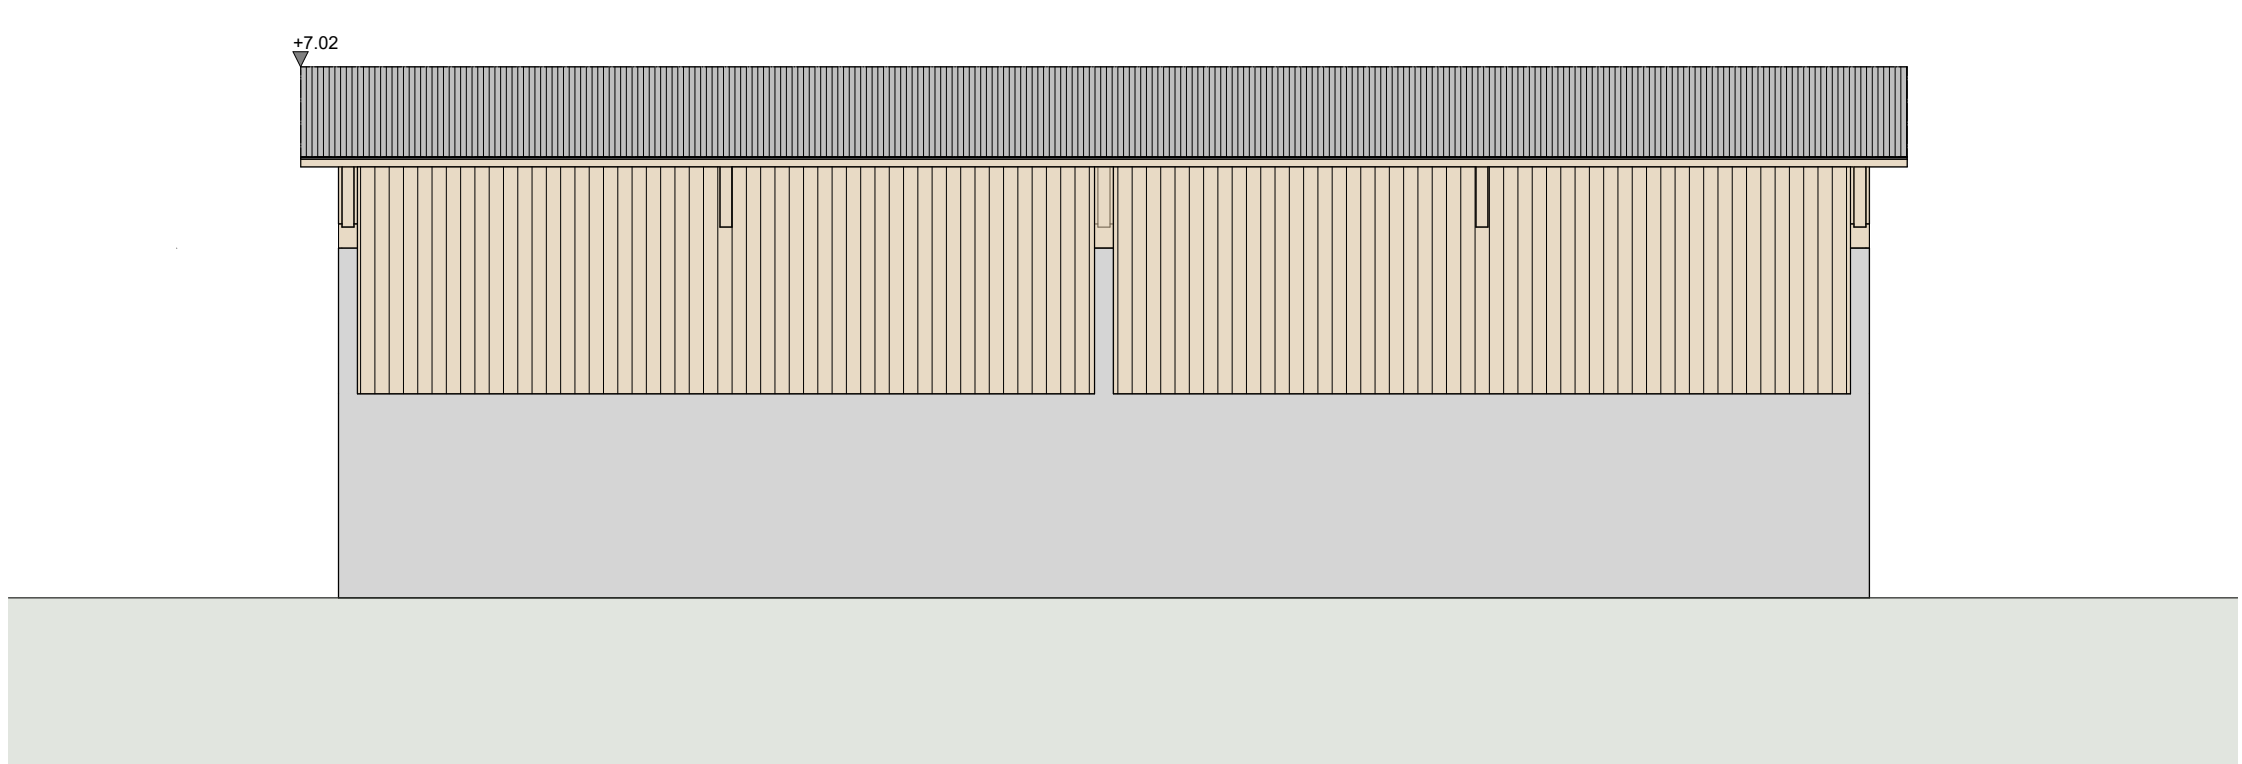

ANSICHT SÜD-OST

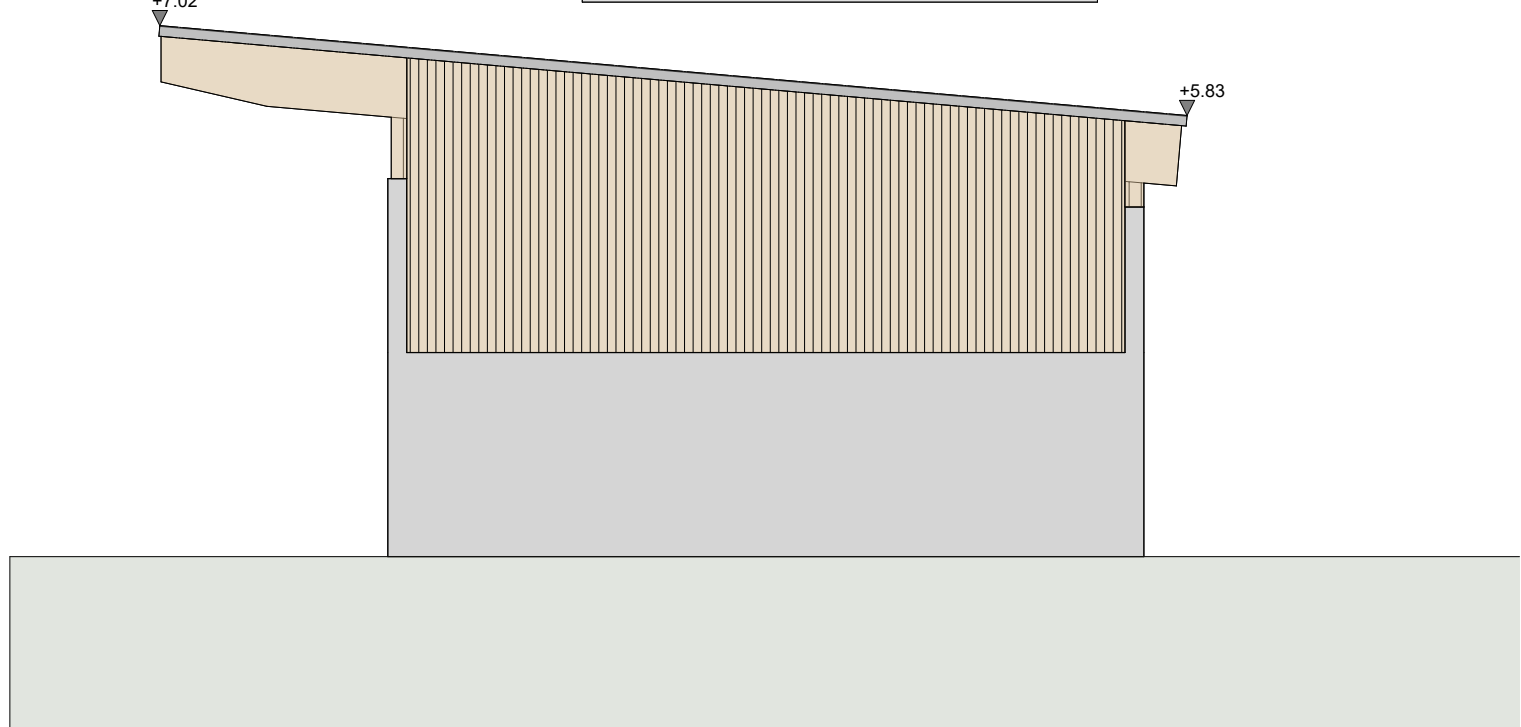

SCHNITT A-A

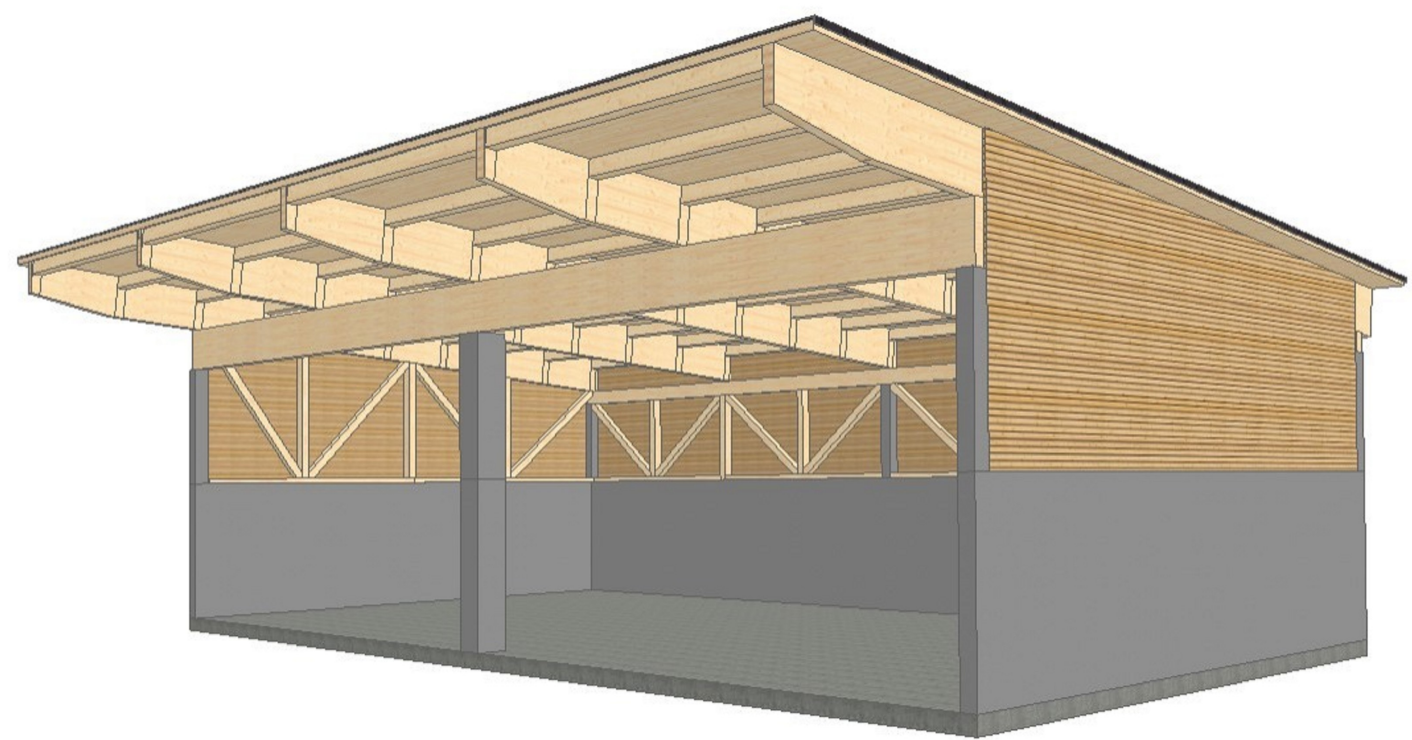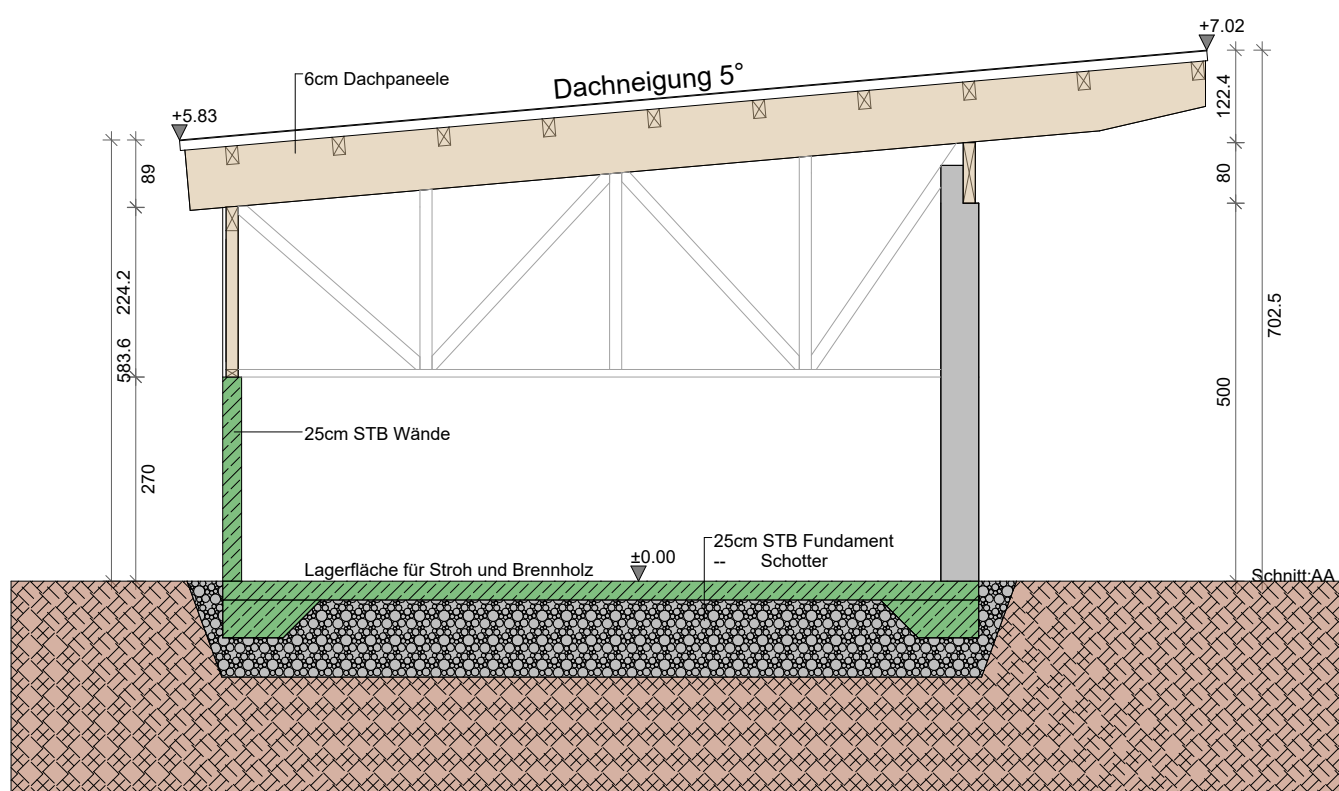

±0,00 BESTAND = ±0,00 NEU

LEGENDE

- Abbruch
- Bestand
- Holzständerwand
- Wohnungstrennwand
- Ziegelmauerwerk
- Stahlbeton
- Holz
- WDVS/Holzweichfaserdämmplatte
- PH Parapethöhe
- FL Fallleitung (AR Ablaufrohr)
- LS Lüftungsschicht
- LL Lüftungsleitung
- BB Regenrohr
- SW Schmutzwasser
- DN Dachneigung
- UZ Unterzug
- Ortswasserleitung
- Strom
- Post/Telekom
- Fäkal Kanal
- Regenwasser
- Grundgrenze
- Baugrenzlinie
- Einfriedung

WICHTIGE HINWEISE:

NATURMASSE NEHMEN, KOTEN KONTROLLIEREN!

KOTEN MIT AUSSTUFUNGEN SIND STÜCKAUSGEWÄHLT!

KOTEN MIT EINER UNTER SIND DURCHGANGSLICHTEN!

ALLE BAUTEILE LT. STATISCHEN ANFORDERUNGEN FUNDAMENTE, WÄNDE, DECKEN, STREGEN, UNTERZÜGE!

FUNDAMENTE AUF TRÄGERLÄNGEN, BOCKEN UND FROSTTIEFEN TESTEN HERSTELLEN!

ES IST DIE GIB RICHTIGKEIT IN IHREN ANZEIGEN FÜR FÜHRUNG ANZEIGEN!

DIE ANGABEN UND AUFBAUEN DES ENERGIEAUSWIRKUNGS SIND EINZUHALTEN!

DER GEGENSTÄNDLICHE EINREICHPLAN DIENT LEDIGLICH DER ERLANGUNG DER BAURECHTLICHEN GENEHMIGUNG UND IST NICHT ALS AUSFÜHRUNGSPLAN ZU VERWENDEN!

Klassifizierungsschlüssel lt. ÖNORM EN 13501-2

K	Tragkonstrukt
F	Feuerschutz
1	Wärmeeinwirkung
W	Strahlung
W	Wärmeeinwirkung gegen Rauch
W	Brandverbreitung
C	Selbstschützende Eigenschaften
S	Rauchschutz
G	Widerstand gegen Kollaps
K	Brandverbreitung
30	Brandverbreitung 30min
60	Brandverbreitung 60min
90	Brandverbreitung 90min
180	Brandverbreitung 180min
R 30	Tragende Bauteile eine Raumabschottung
R 30	Tragende Bauteile mit Rauchschutz
F, 30°C	Feuerschutz mit Schmelzvorrichtung
F	RAUCHWÄRMELER
F	TRAGBAHRE FEUERLÖSCHER lt. TRVB 124

EINREICHPLAN

NEUBAU EINER LANDW. GENUTZTEN HALLE FÜR DIE LAGERUNG VON STROH UND HOLZ SOWIE ERRICHTUNG EINER SICKERMULDE

8274 Unterdombach - Unterdombach 14 - Halle

Grst.Nr. 34/1 | EZ 21 | KG 64150 Unterdombach

BEHÖRDE

BAUFÜHRER

PLANUNG

Nöhner Rene
Unterdombach 14
8274 Buch- St. Magdalena

BAUWERBER

Nöhner Rene
Unterdombach 14
8274 Buch- St. Magdalena

GRUNDEIGENTÜMER

Holz & Bau Hubsch-Baumhaus

HHH

PLANUNG

ANSICHTEN M 1:100

GRUNDRISS, SCHNITT M 1:100

LAGEPLAN M 1:500 u. 1:1000

ZEICHNER HT

PLANNUMMER ent_18122024

DATUM 18.12.2024